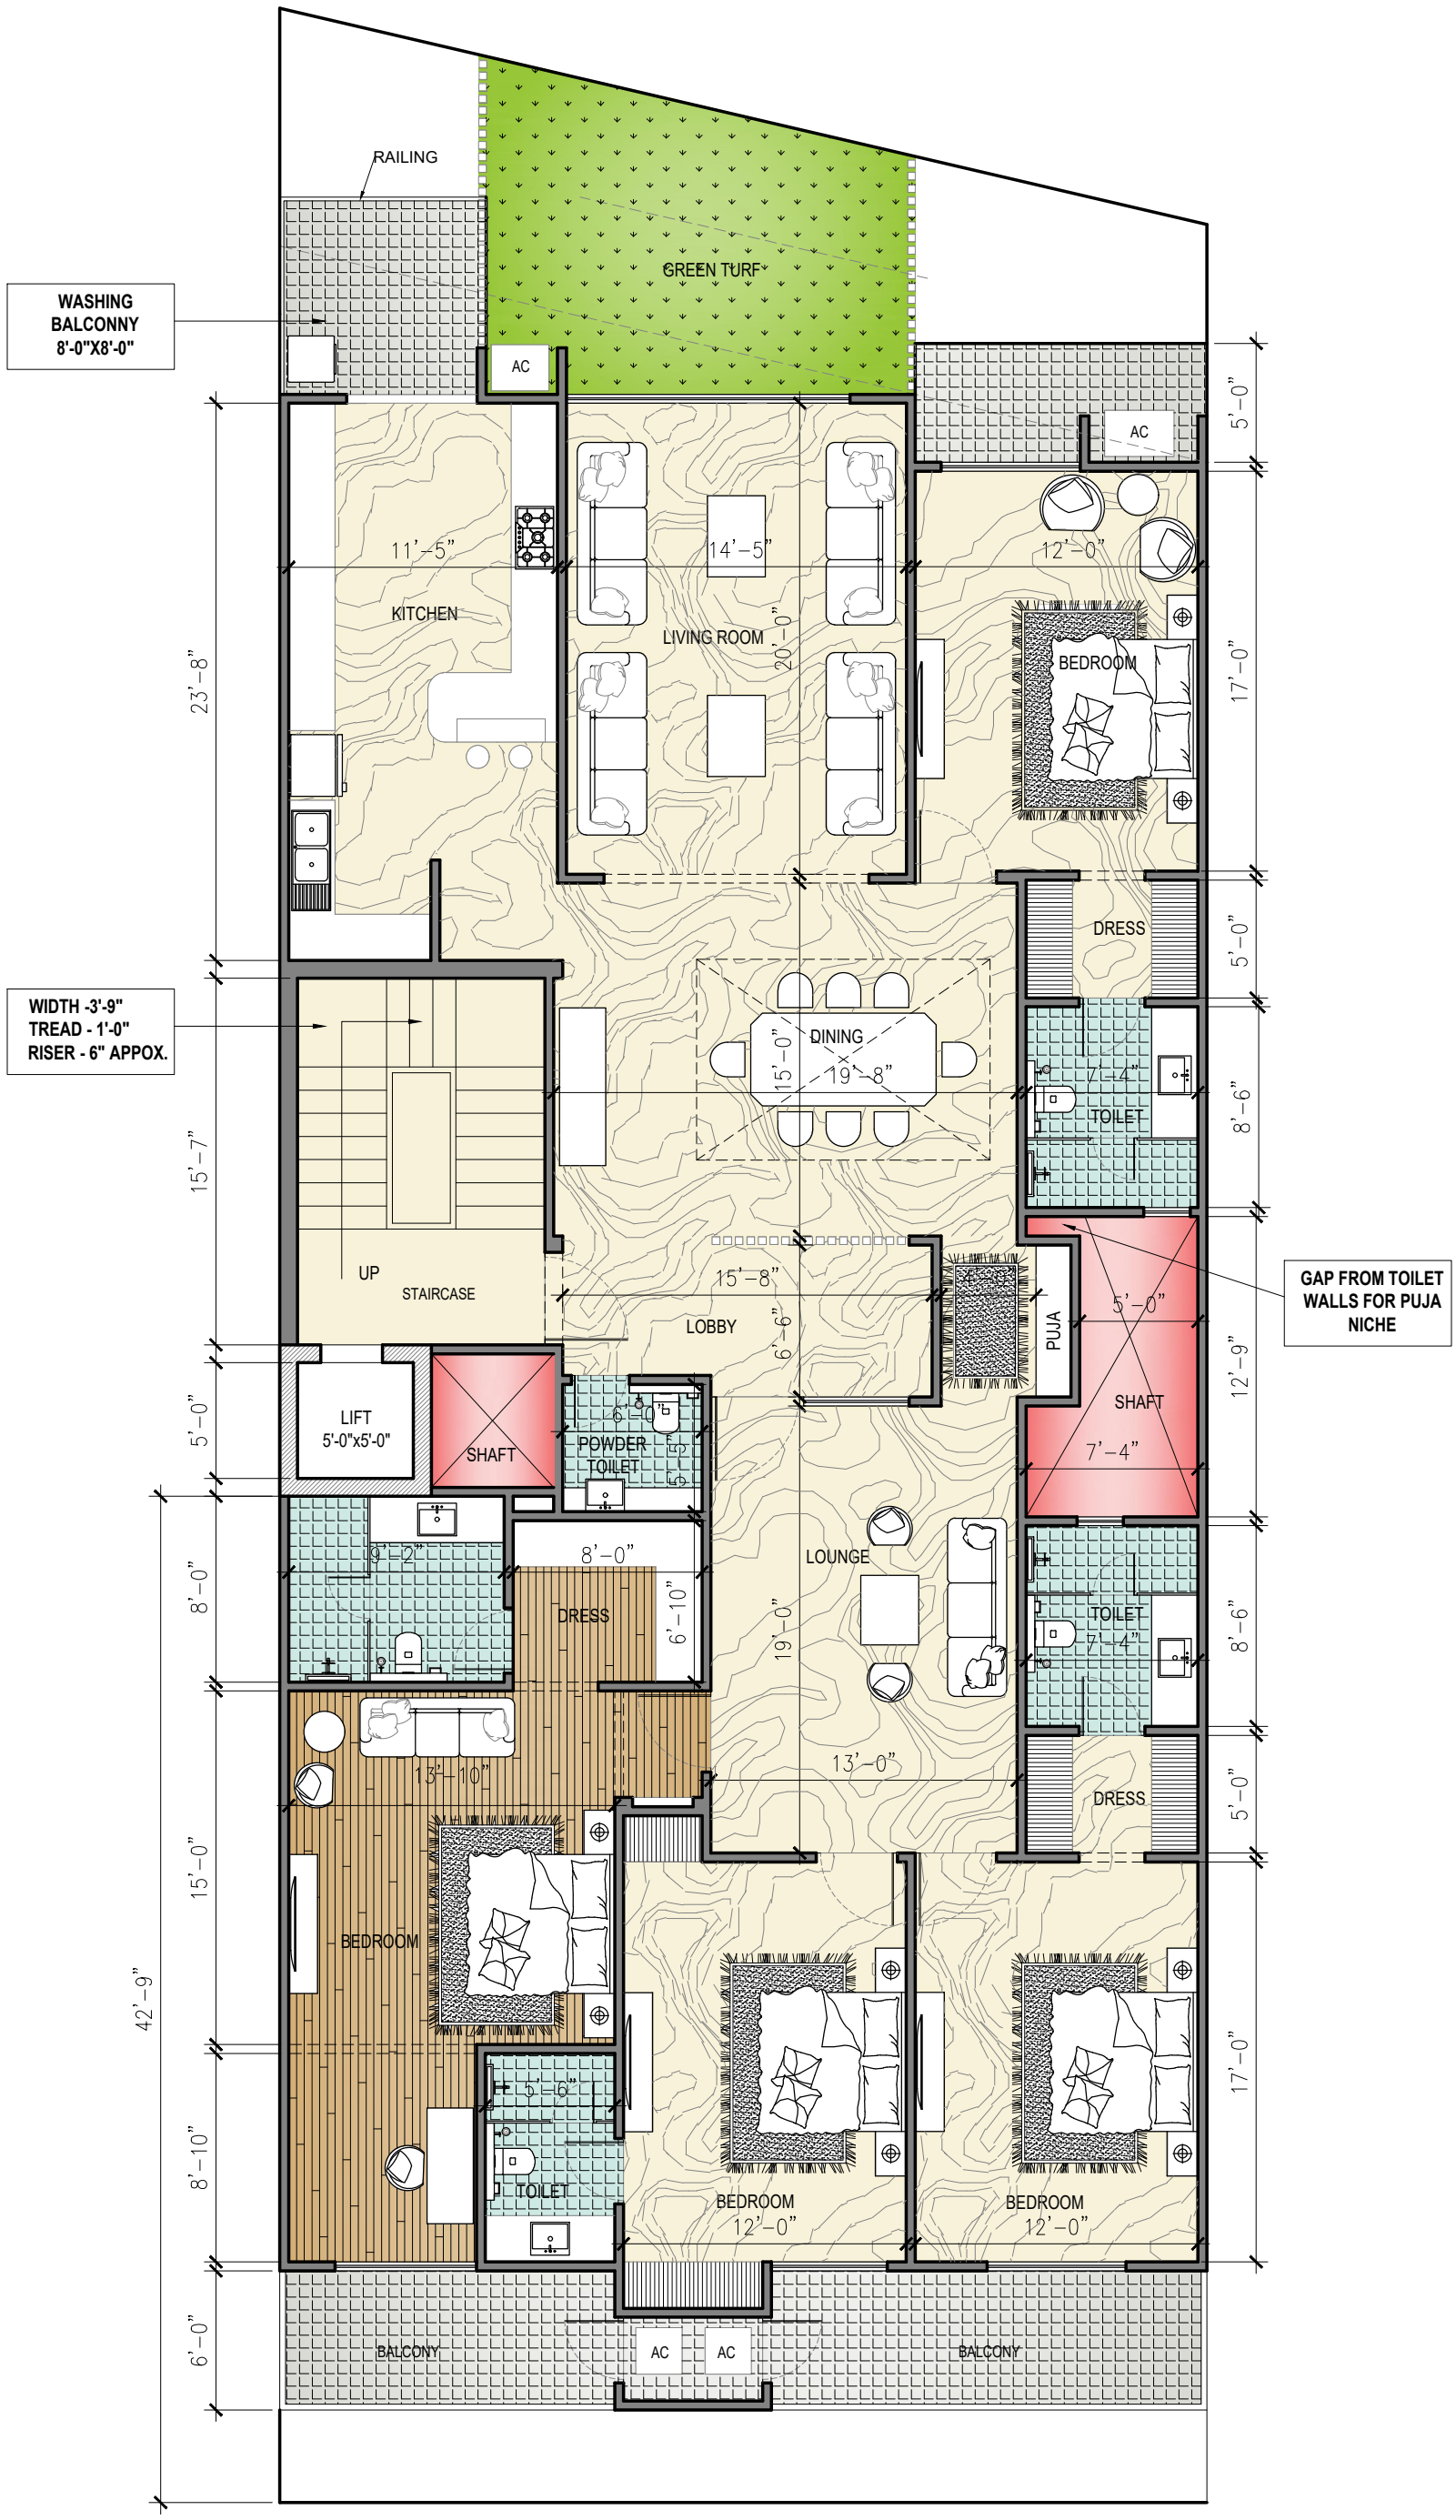
RAILING
GREEN TURF
WASHING BALCONNY 8'-0"X8'-0"
AC
AC
5'-0"
11'-5"
14'-5"
12'-0"
KITCHEN
LIVING ROOM
20'-0"
BEDROOM
17'-0"
23'-8"
DRESS
5'-0"
WIDTH -3'-9"
TREAD - 1'-0"
RISER - 6" APPOX.
DINING
15'-0"
19'-8"
7'-4"
TOILET
8'-6"
15'-7"
UP
STAIRCASE
15'-8"
LOBBY
6'-6"
PUJA
5'-0"
GAP FROM TOILET WALLS FOR PUJA NICHE
12'-9"
LIFT 5'-0"x5'-0"
SHAFT
POWDER TOILET
6'-0"
5'-5"
SHAFT
7'-4"
5'-0"
9'-2"
8'-0"
DRESS
6'-10"
LOUNGE
19'-0"
TOILET
7'-4"
8'-6"
8'-0"
13'-10"
13'-0"
DRESS
5'-0"
15'-0"
BEDROOM
42'-9"
5'-6"
TOILET
8'-10"
BEDROOM
12'-0"
BEDROOM
12'-0"
17'-0"
6'-0"
BALCONY
AC
AC
BALCONY